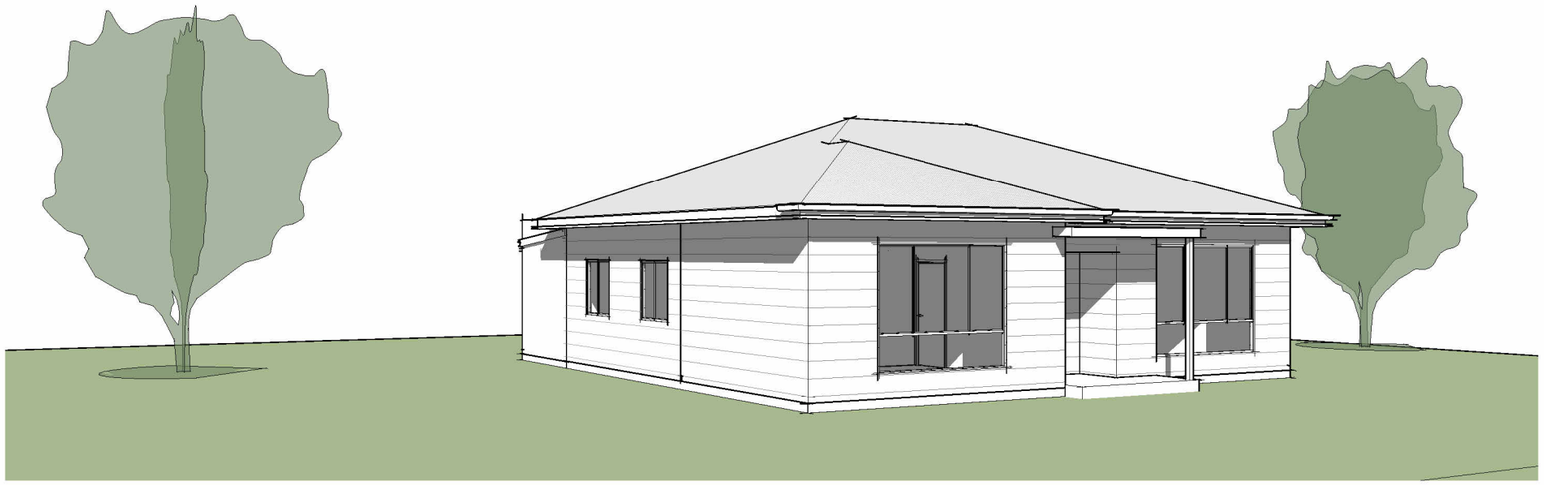

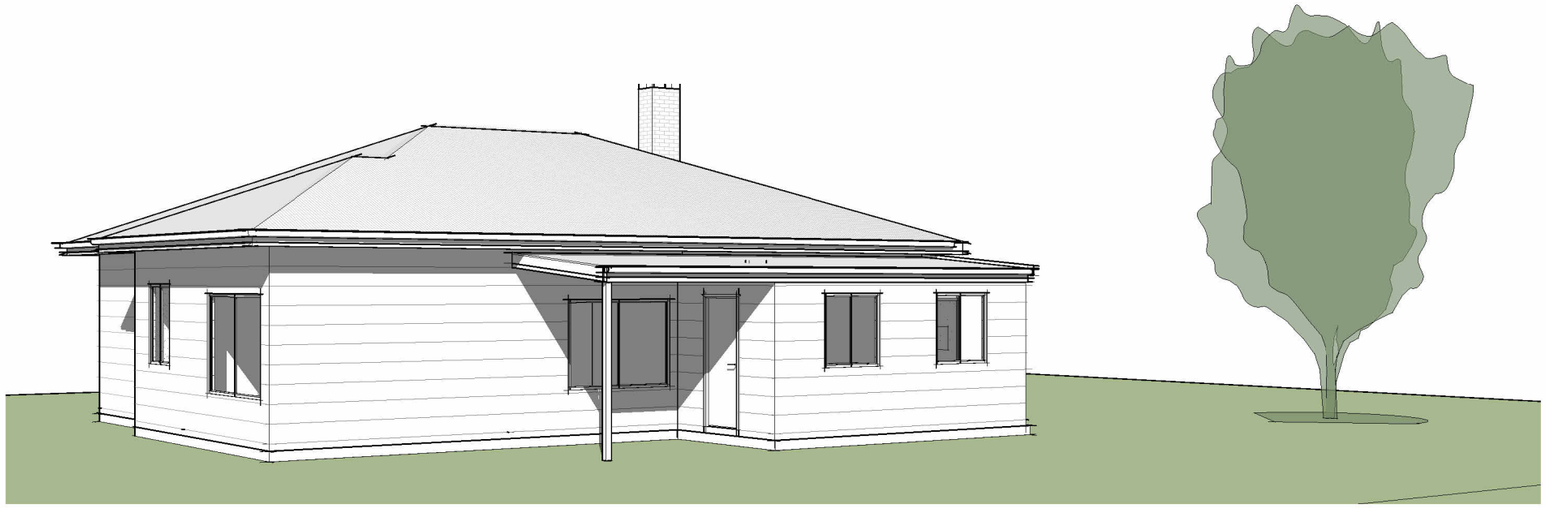

EXISTING

PROPOSAL:	ADDRESS:	REVISION:	DRAWN:	DATE:	DWG NO:
PROPOSED EXTENSION		04/06/2025 CONCEPT SKETCH 11/07/2025 PRELIMINARY PLANS		04/06/2025	**A1-00**

NOT FOR CONSTRUCTION

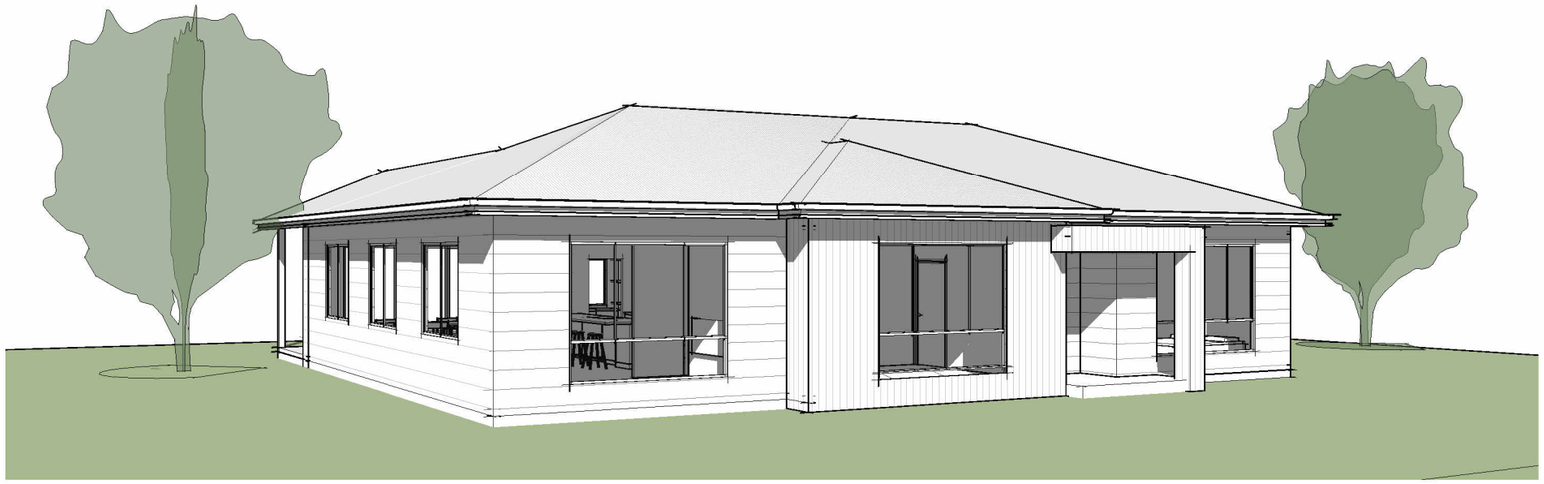

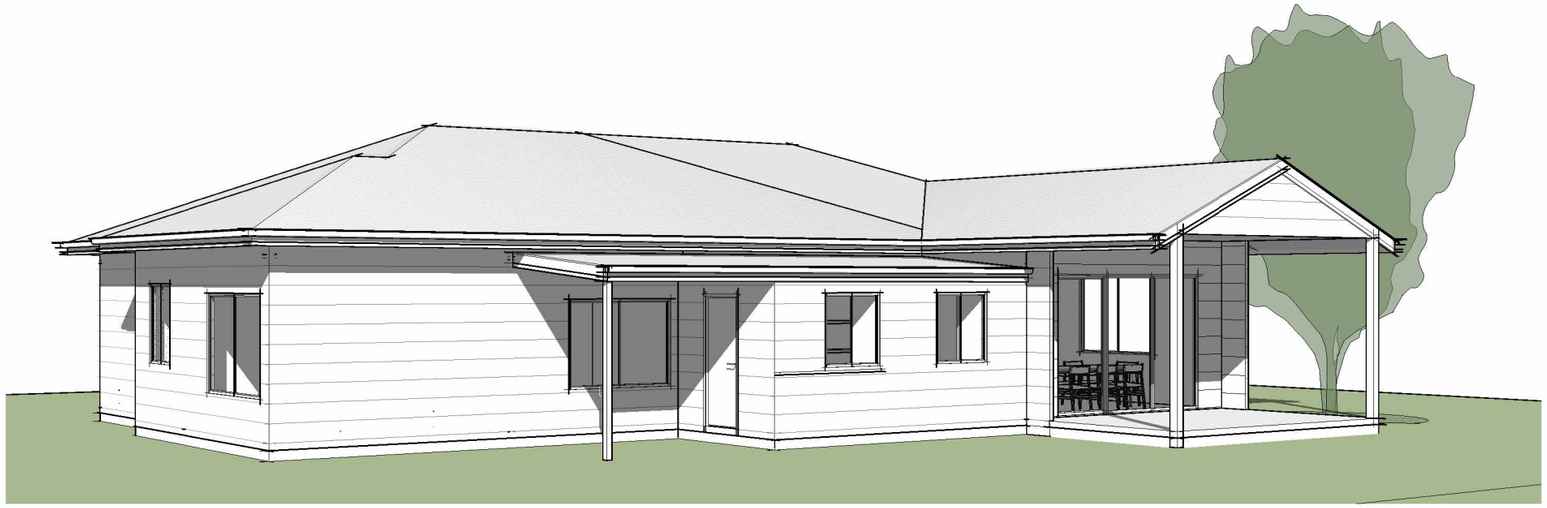

PROPOSED

PROPOSAL:	ADDRESS:	REVISION:	DRAWN:	DATE:	DWG NO:
PROPOSED EXTENSION		04/06/2025 CONCEPT SKETCH 11/07/2025 PRELIMINARY PLANS		04/06/2025	**A1-01**

NOT FOR CONSTRUCTION

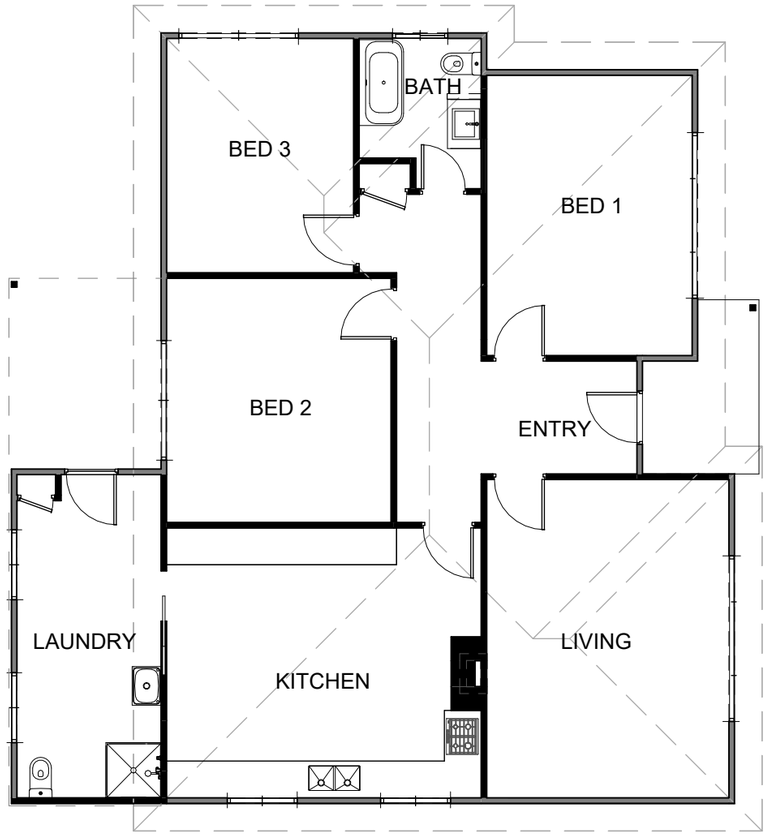

EXISTING FLOOR PLAN

1 : 100

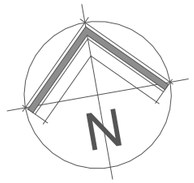

PROPOSAL:	ADDRESS:	REVISION:	DRAWN:	DATE:	DWG NO:
PROPOSED EXTENSION		04/06/2025 CONCEPT SKETCH 11/07/2025 PRELIMINARY PLANS		04/06/2025	A1-02

NOT FOR CONSTRUCTION

EXISTING EAST ELEVATION

1 : 100

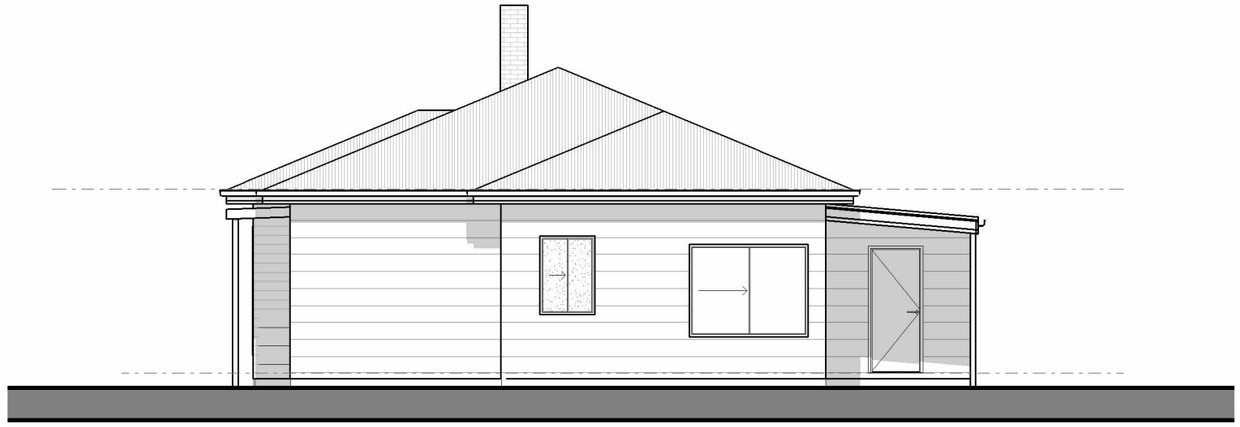

EXISTING NORTH ELEVATION

1 : 100

EXISTING WEST ELEVATION

1 : 100

EXISTING SOUTH ELEVATION

1 : 100

PROPOSAL:	ADDRESS:	REVISION:	DRAWN:	DATE:	DWG NO:
PROPOSED EXTENSION		04/06/2025 CONCEPT SKETCH 11/07/2025 PRELIMINARY PLANS		04/06/2025	**A1-03**

NOT FOR CONSTRUCTION

Demolition Method Statement
- Disconnect all services, power, water, gas etc.
- Locate stormwater and sewer drains and seal at points of discharge.
- Protect adjoining property
- Provide temporary wall bracing where required.
- Remove tiled roof ,Fascia ,Gutter and down pipes (where required)
- Remove any internal linings.
- Remove loose or attached fittings and built-in fixtures, internally and externally.
- Remove brick work from the top course of bricks down (where required)
- Place bricks in building skip that is provided
- Clean up site.
- Fill in excavations.
- Check for any hazards.
- Clean site entry points and infrastructure where necessary.
- Retained fabric will be safegaurded during demolition and construction (structurally propped, weatherproofed and not damaged)

REMOVE ALL EXISTING JOINERY & FIXTURES TO BATH & MAKE GOOD TO ALL ADJACENT SURFACES

DEMOLISH EXTERNAL WALL WHERE REQUIRED
MAKE GOOD TO ALL ADJACENT SURFACES

REMOVE ALL EXISTING JOINERY & FIXTURES TO KITCHEN, L'DRY AND WC

REMOVE EXISTING WINDOWS & DEMOLISH EXTERNAL WALL WHERE REQUIRED
MAKE GOOD TO ALL ADJACENT SURFACES

DEMOLISH PART OF EXISTING ROOFING & ROOFING STRUCTURE.
MAKE GOOD TO ALL ADJACENT SURFACES
(SHOWN IN RED DIAGONAL HATCH)

REMOVE EXISTING INTERNAL DOORS & DEMOLISH EXISTING WALLS WHERE SHOWN
MAKE GOOD TO ALL ADJACENT SURFACES

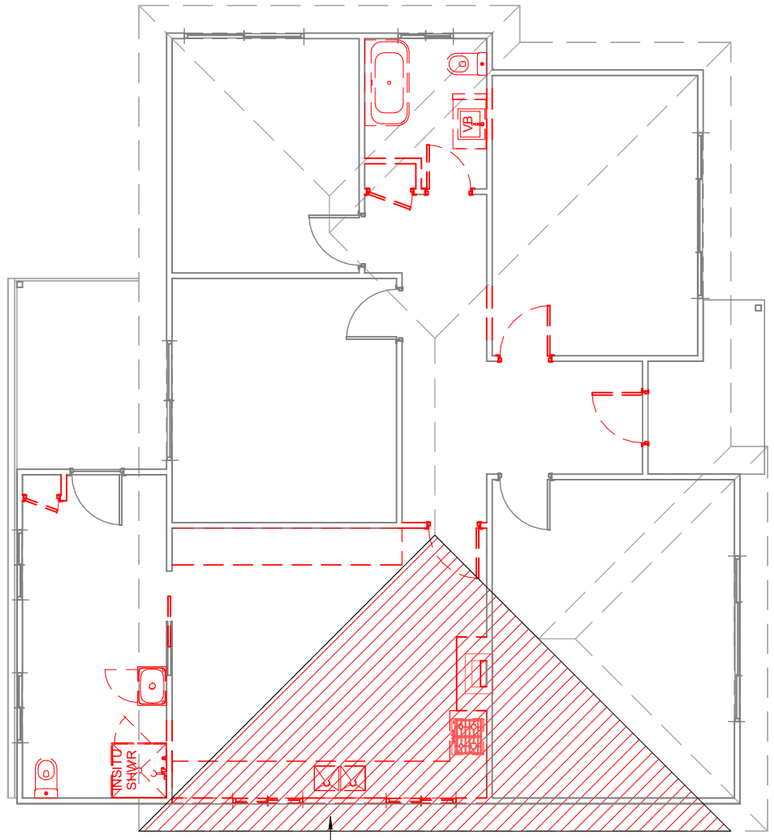

NOTE: PROP-UP EXISTING ROOFING WHERE REQUIRED PRIOR DEMOLITION OF EXTERNAL WALLS
REFER TO ENGINEER FOR LOAD BEARING REQUIREMENTS

DEMO PLAN

1 : 100

DENOTES EXISTING WALLS

DENOTES WALLS TO BE DEMOLISHED

NOTE; PROP-UP EXISTING ROOFING WHERE REQUIRED PRIOR DEMOLITION OF EXTERNAL WALLS

PROPOSAL:	ADDRESS:	REVISION:	DRAWN:	DATE:	DWG NO:
PROPOSED EXTENSION		04/06/2025 CONCEPT SKETCH 11/07/2025 PRELIMINARY PLANS		04/06/2025	**A1-04**

NOT FOR CONSTRUCTION

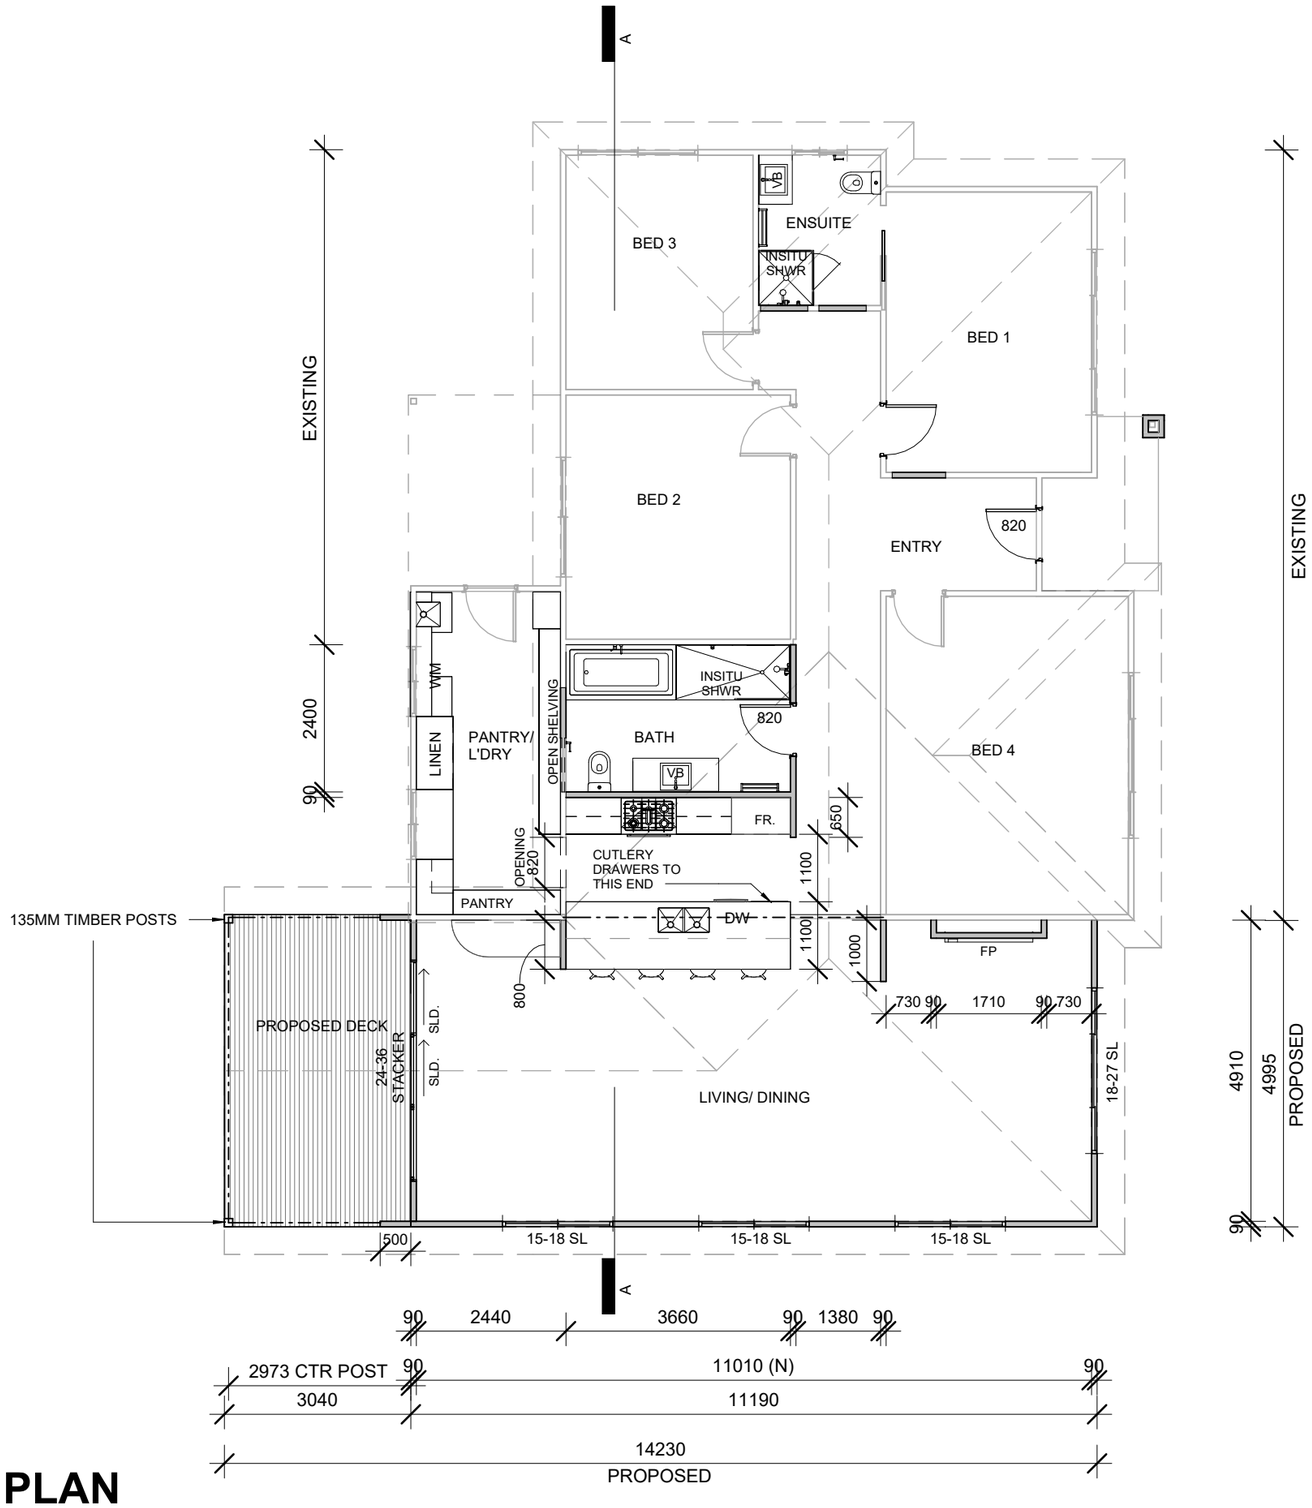

PROPOSED FLOOR PLAN

1 : 100

PROPOSAL:	ADDRESS:	REVISION:	DRAWN:	DATE:	DWG NO:
PROPOSED EXTENSION		04/06/2025 CONCEPT SKETCH 11/07/2025 PRELIMINARY PLANS		04/06/2025	A1-05

NOT FOR CONSTRUCTION

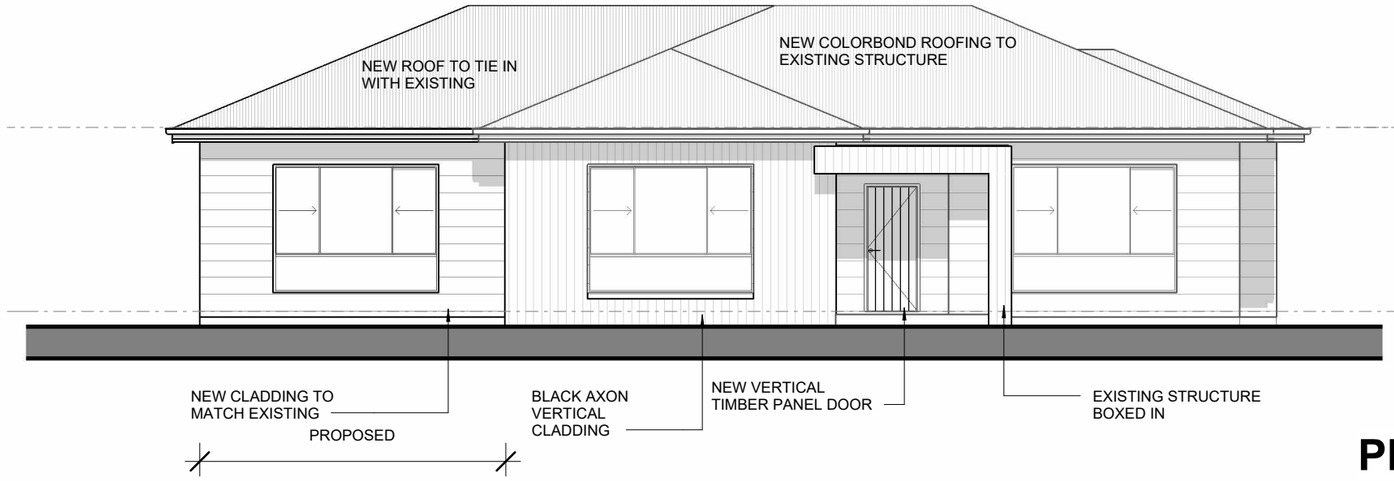

PROPOSED EAST ELEVATION

1 : 100

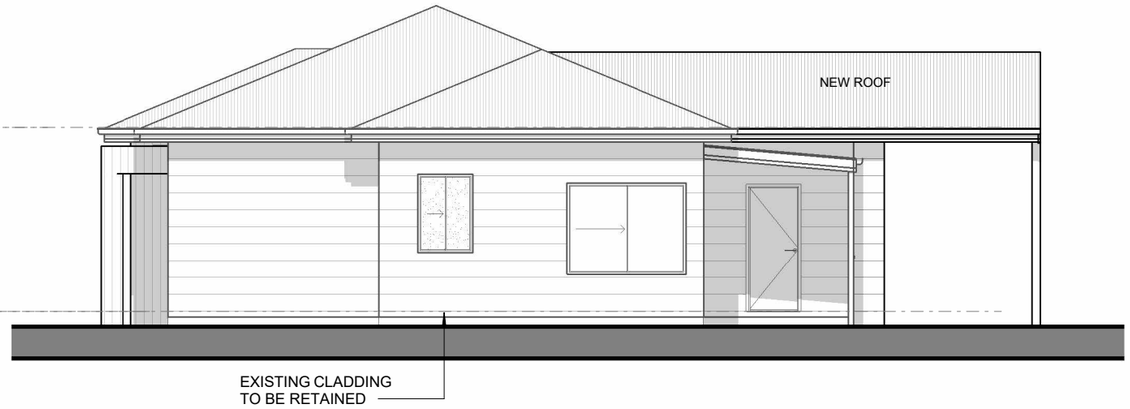

PROPOSED NORTH ELEVATION

1 : 100

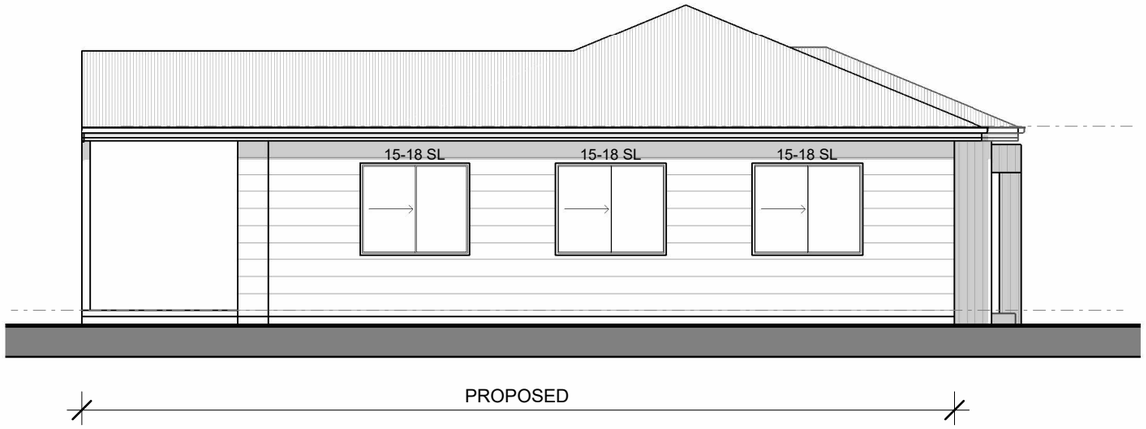

PROPOSED SOUTH ELEVATION

1 : 100

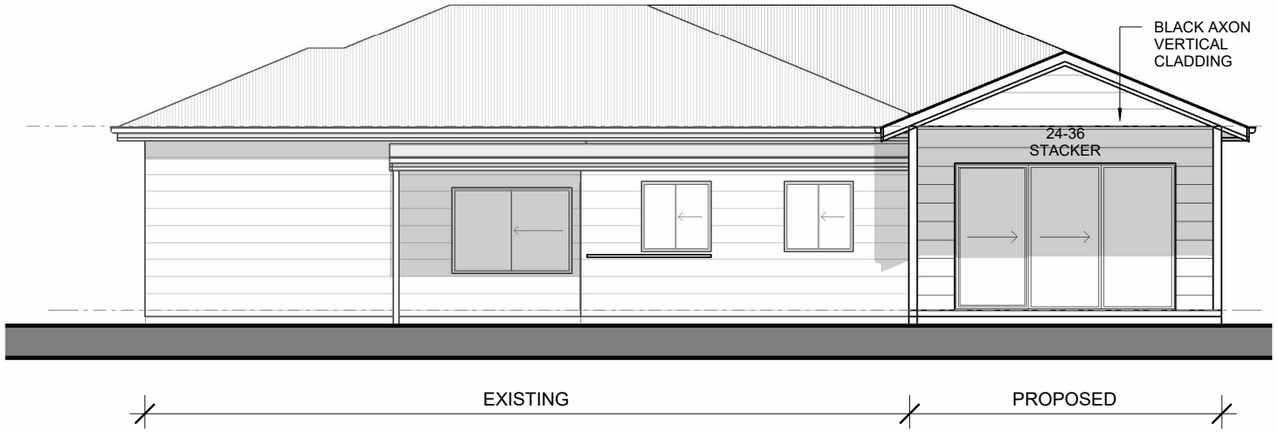

PROPOSED WEST ELEVATION

1 : 100

PROPOSAL:	ADDRESS:	REVISION:	DRAWN:	DATE:	DWG NO:
PROPOSED EXTENSION		04/06/2025 CONCEPT SKETCH 11/07/2025 PRELIMINARY PLANS		04/06/2025	**A1-06**

NOT FOR CONSTRUCTION

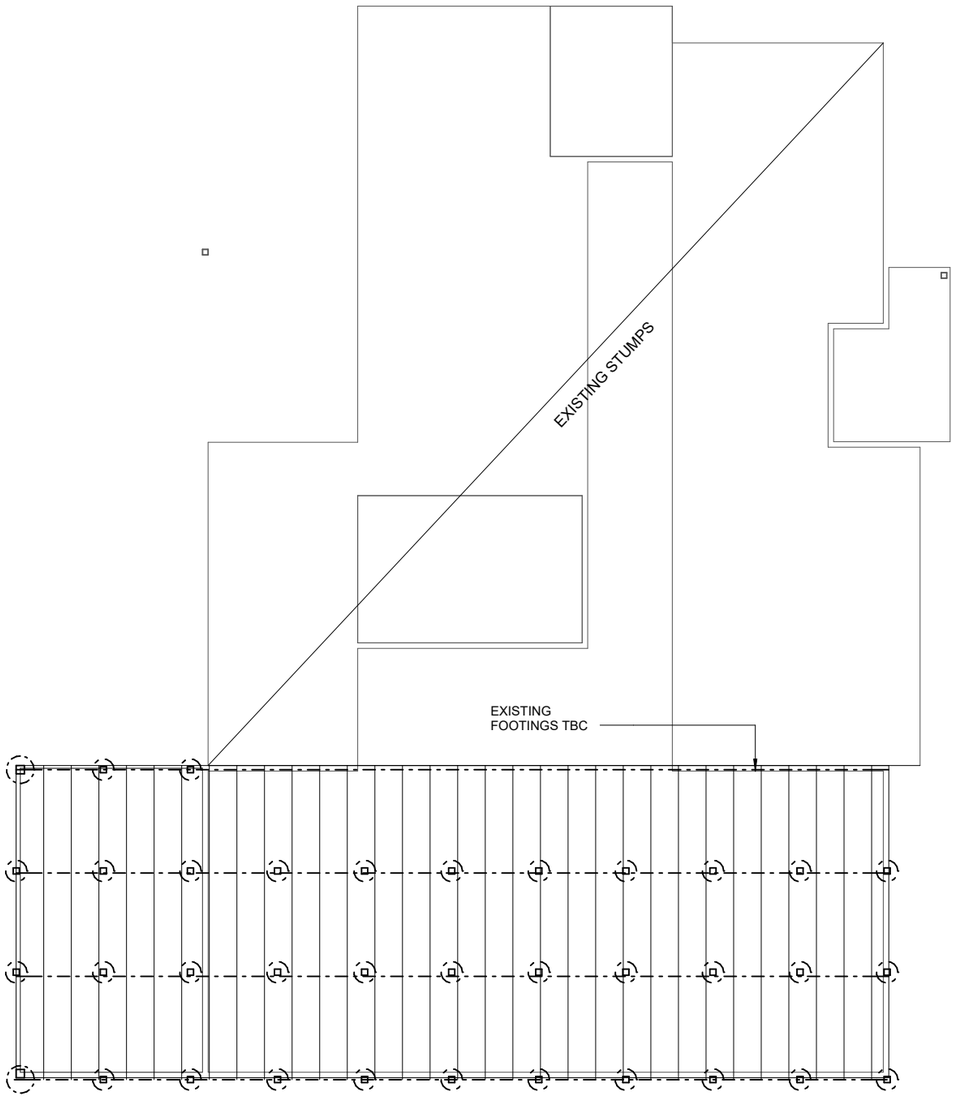

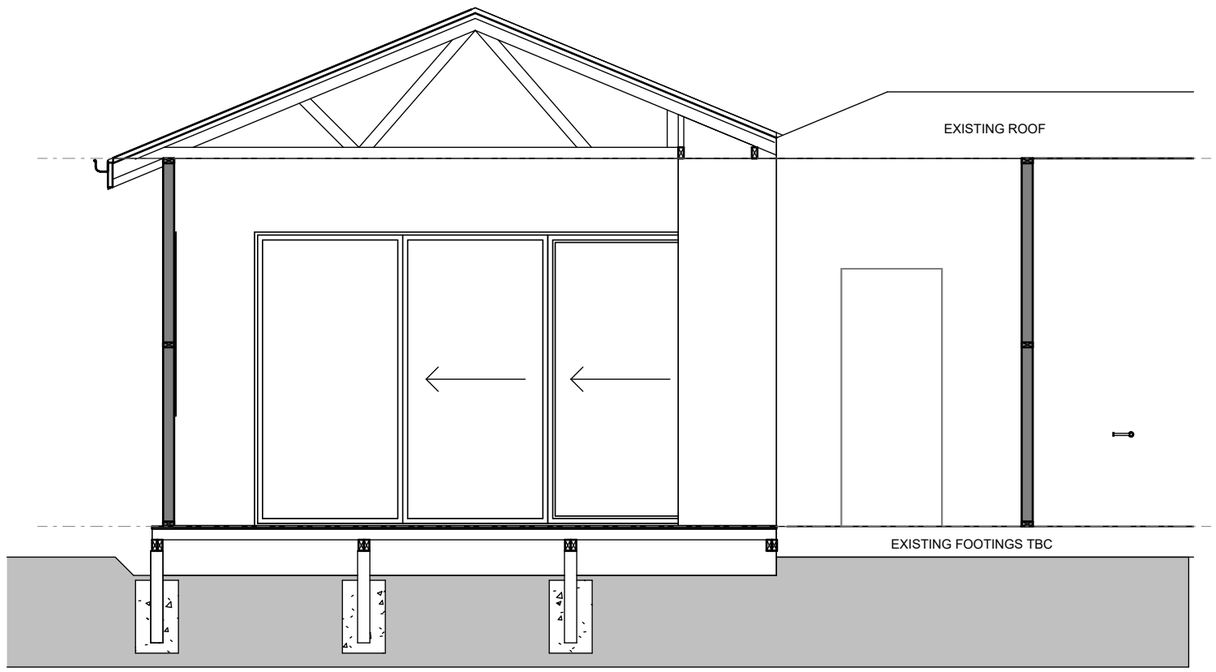

SUB FLOOR CONSTRUCTION
SELECTED FLOORING ON 90X45 LVL
JOISTS @ 450CTS ON 2/90X45 LVL
BEARERS @ MAXIMUM 1600 SPACING.
REFER TO ENGINEER SPECS FOR CONFIRMATION OF TIMBER CALCULATIONS.

STRUCTURAL FLOORING PLAN

1 : 100

SECTION A-A

1 : 50

PROPOSAL:	ADDRESS:	REVISION:	DRAWN:	DATE:	DWG NO:
PROPOSED EXTENSION		04/06/2025 CONCEPT SKETCH 11/07/2025 PRELIMINARY PLANS		04/06/2025	**A1-07**

NOT FOR CONSTRUCTION

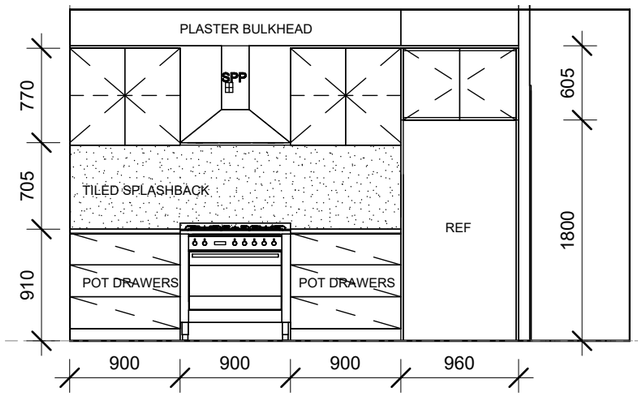

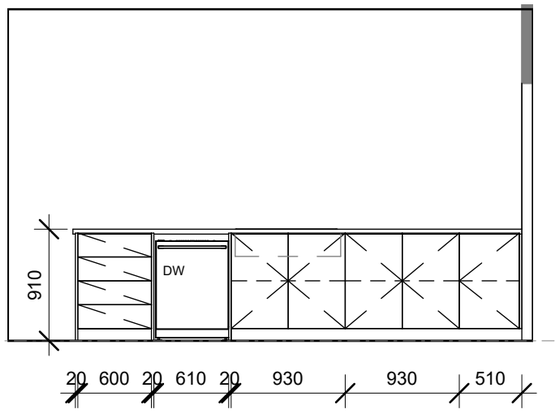

KITCHEN

1 : 50

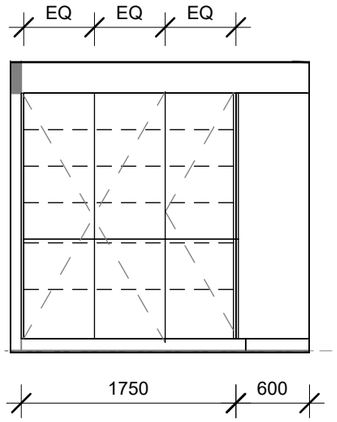

PANTRY

1 : 50

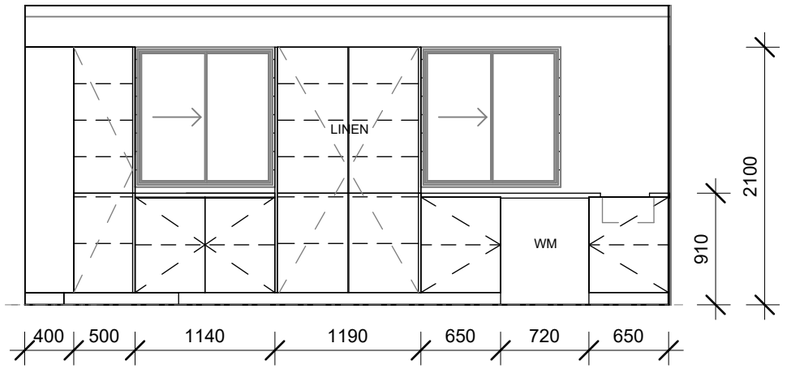

LAUNDRY A

1 : 50

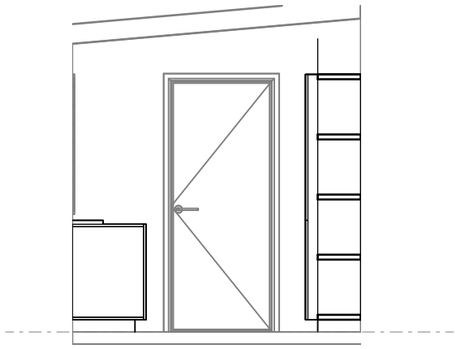

LAUNDRY B

1 : 50

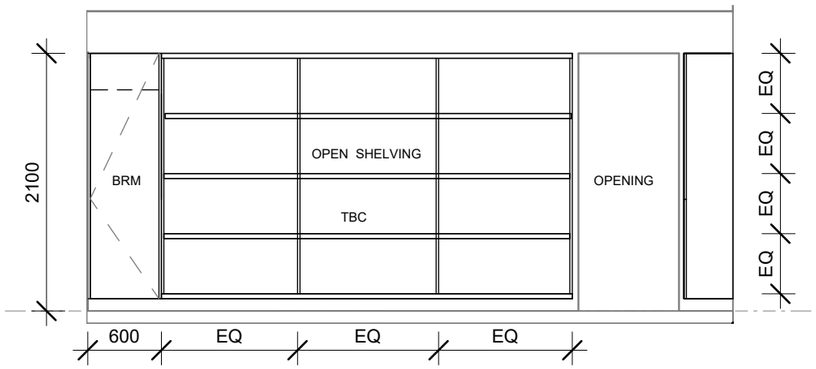

LAUNDRY C

1 : 50

PROPOSAL:	ADDRESS:	REVISION:	DRAWN:	DATE:	DWG NO:
PROPOSED EXTENSION		04/06/2025 CONCEPT SKETCH 11/07/2025 PRELIMINARY PLANS		04/06/2025	A1-08

NOT FOR CONSTRUCTION

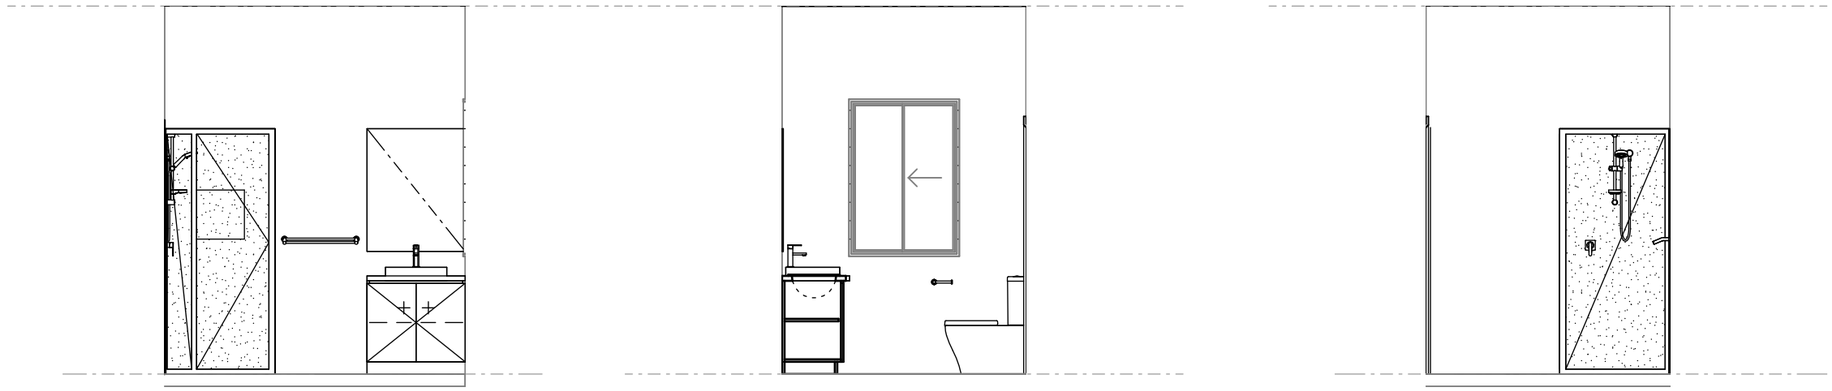

ENSUITE

1 : 50

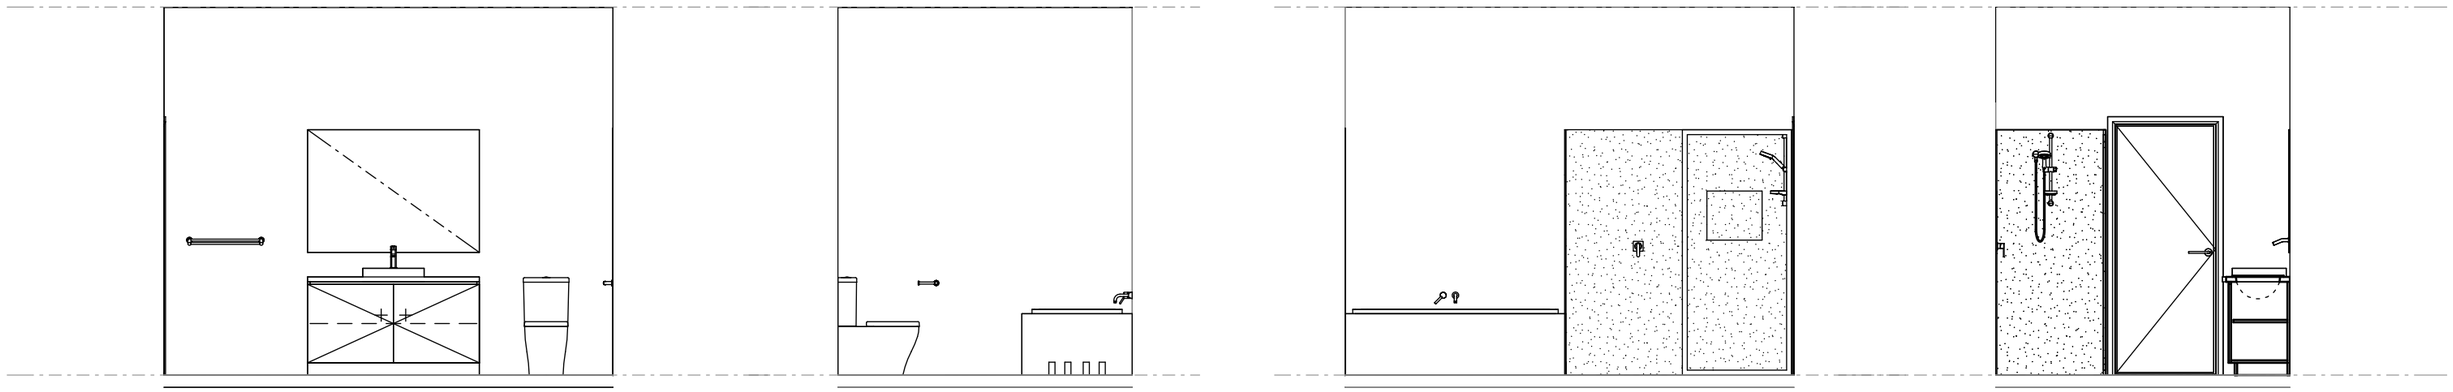

BATHROOM

1 : 50

PROPOSAL:	ADDRESS:	REVISION:	DRAWN:	DATE:	DWG NO:
PROPOSED EXTENSION		04/06/2025 CONCEPT SKETCH 11/07/2025 PRELIMINARY PLANS		04/06/2025	**A1-09**

NOT FOR CONSTRUCTION