Address: REDACTED		**Design:** PROPOSED RENOVATION		Amendments		Date	Description
				Date	Description		
Client:				13/08/2025	CONCEPT SKETCH		
Date	13/08/2025	Page Size	A3				
Page Number	1.0 3D	Drawings Prepared By	ND				

NOT FOR CONSTRUCTION

Address: REDACTED		**Design:** PROPOSED RENOVATION		Amendments		Date	Description
				Date	Description		
				13/08/2025	CONCEPT SKETCH		
Client:							
Date	13/08/2025	Page Size	A3				
Page Number	1.1 3D NEW	Drawings Prepared By	ND				

NOT FOR CONSTRUCTION

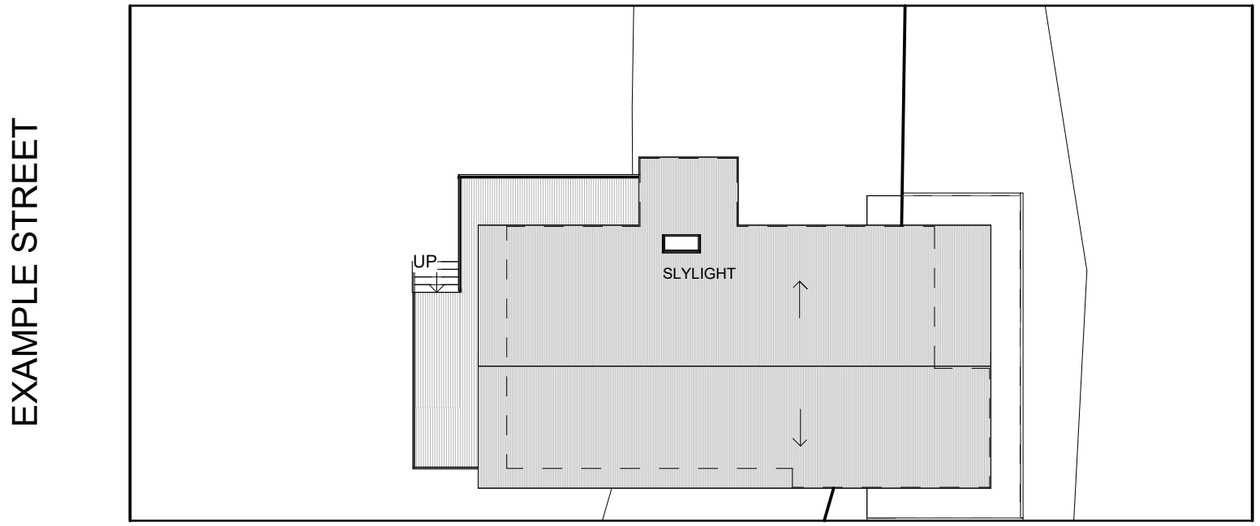

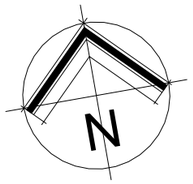

APPROX SITE PLAN

1 : 200

Address: REDACTED		**Design:** PROPOSED RENOVATION		Amendments		Date	Description
				Date	Description		
				13/08/2025	CONCEPT SKETCH		
Client:							
Date	13/08/2025	Page Size	A3 1 : 200				
Page Number	2.0 SITE	Drawings Prepared By	ND				

NOT FOR CONSTRUCTION

EXISTING FLOOR PLAN

1 : 100

Address: REDACTED		**Design:** PROPOSED RENOVATION		Amendments		Date	Description
				Date	Description		
Client:				13/08/2025	CONCEPT SKETCH		
Date	13/08/2025	Page Size	A3 1 : 100				
Page Number	3.0 EXISTING FLOOR PLAN	Drawings Prepared By	ND				

NOT FOR CONSTRUCTION

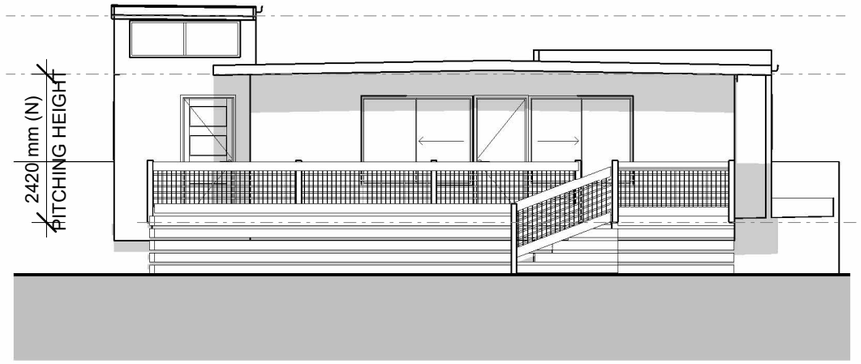

EAST ELEVATION - EXISTING

1 : 100

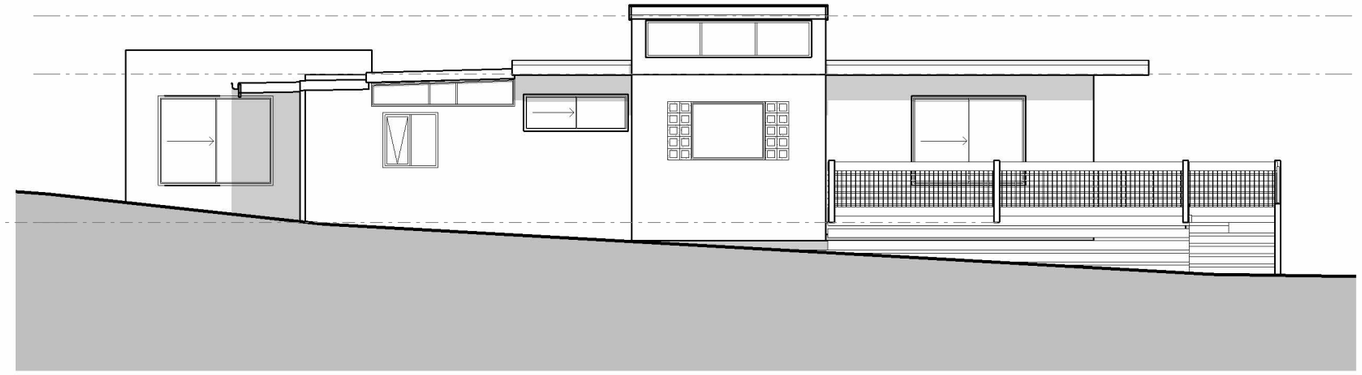

SOUTH ELEVATION - EXISTING

1 : 100

WEST ELEVATION - EXISTING

1 : 100

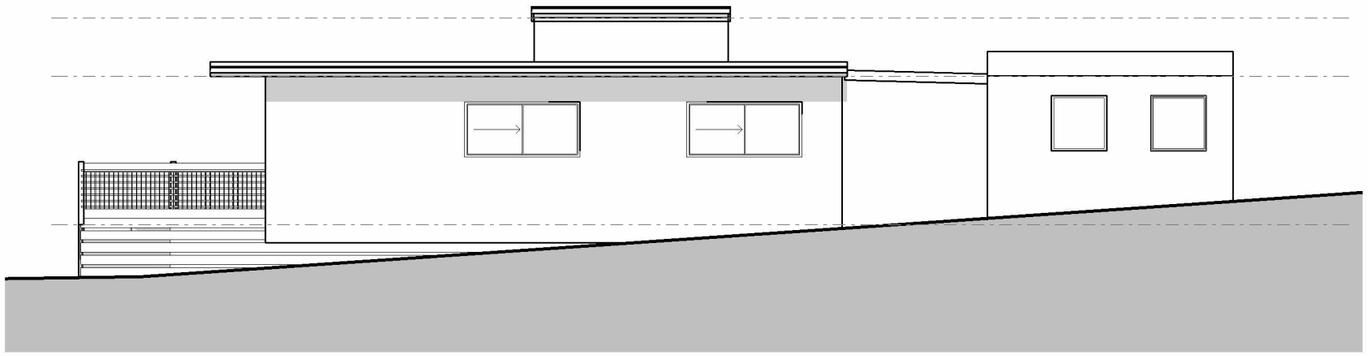

NORTH ELEVATION - EXISTING

1 : 100

Address: REDACTED		**Design:** PROPOSED RENOVATION		Amendments		Date	Description
				Date	Description		
Client:				13/08/2025	CONCEPT SKETCH		
Date	13/08/2025	Page Size	A3 1 : 100				
Page Number	3.1 EXISTING ELEVATIONS	Drawings Prepared By	ND				

NOT FOR CONSTRUCTION

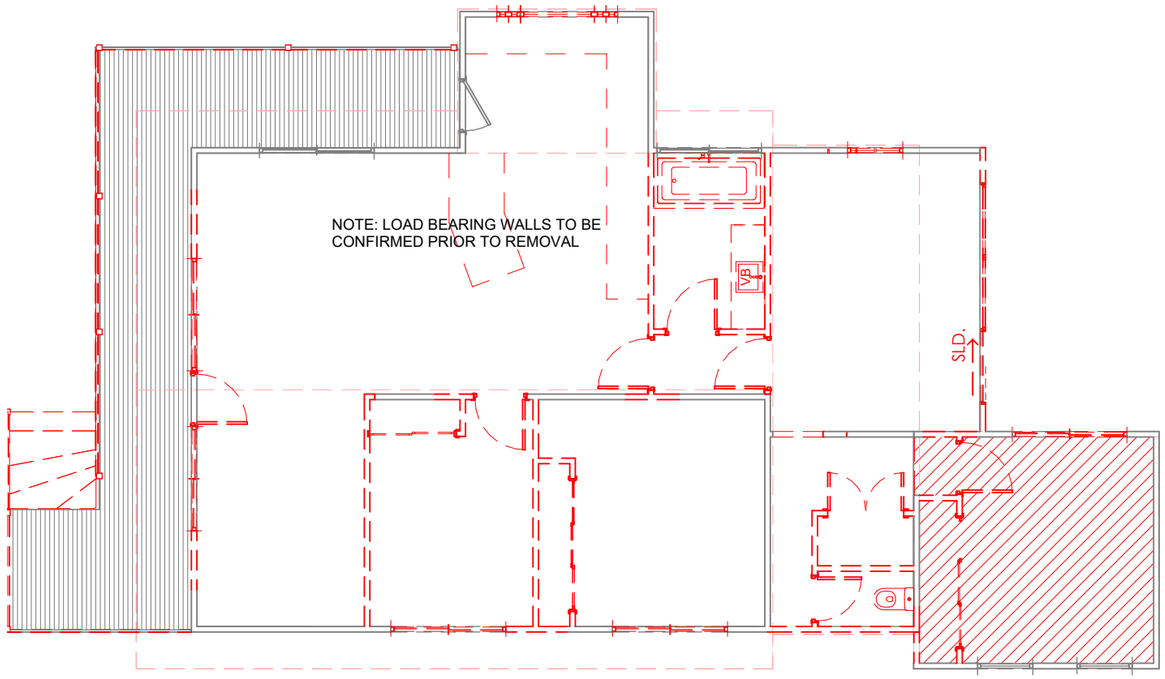

DENOTES EXISTING WALLS

DENOTES WALLS TO BE DEMOLISHED

Demolition Method Statement
- Disconnect all services, power, water, gas etc.
- Locate stormwater and sewer drains and seal at points of discharge.
- Protect adjoining property
- Provide temporary wall bracing where required.
- Remove tiled roof ,Fascia ,Gutter and down pipes (where required)
- Remove any internal linings.
- Remove loose or attached fittings and built-in fixtures, internally and externally.
- Remove brick work from the top course of bricks down (where required)
- Place bricks in building skip that is provided
- Clean up site.
- Fill in excavations.
- Check for any hazards.
- Clean site entry points and infrastructure where necessary.
- Retained fabric will be safegaurded during demolition and construction (structurally propped, weatherproofed and not damaged)

DEMOLISH EXISTING DECK

REMOVE ALL EXISTING JOINERY & FIXTURES TO BATH & MAKE GOOD TO ALL ADJACENT SURFACES

DEMOLISH EXTERNAL WALL WHERE REQUIRED
MAKE GOOD TO ALL ADJACENT SURFACES

REMOVE ALL EXISTING JOINERY & FIXTURES TO KITCHEN, L'DRY AND WC

REMOVE EXISTING WINDOWS & DEMOLISH EXTERNAL WALL WHERE REQUIRED
MAKE GOOD TO ALL ADJACENT SURFACES

NOTE; PROP-UP EXISTING ROOFING WHERE REQUIRED PRIOR DEMOLITION OF EXTERNAL WALLS

DEMOLISH PART OF EXISTING ROOFING & ROOFING STRUCTURE.
MAKE GOOD TO ALL ADJACENT SURFACES
(SHOWN IN RED DIAGONAL HATCH)

REMOVE EXISTING INTERNAL DOORS & DEMOLISH EXISTING WALLS WHERE SHOWN
MAKE GOOD TO ALL ADJACENT SURFACES

DEMOLISH PART OF EXISTING ROOFING & ROOFING STRUCTURE.
MAKE GOOD TO ALL ADJACENT SURFACES
(SHOWN IN RED DIAGONAL HATCH)

DEMO PLAN

1 : 100

Address: REDACTED		**Design:** PROPOSED RENOVATION	
Client:			
Date	13/08/2025	Page Size	A3 1 : 100
Page Number	4.0 DEMO	Drawings Prepared By	ND

Amendments		Date	Description
Date	Description		
13/08/2025	CONCEPT SKETCH		

NOT FOR CONSTRUCTION

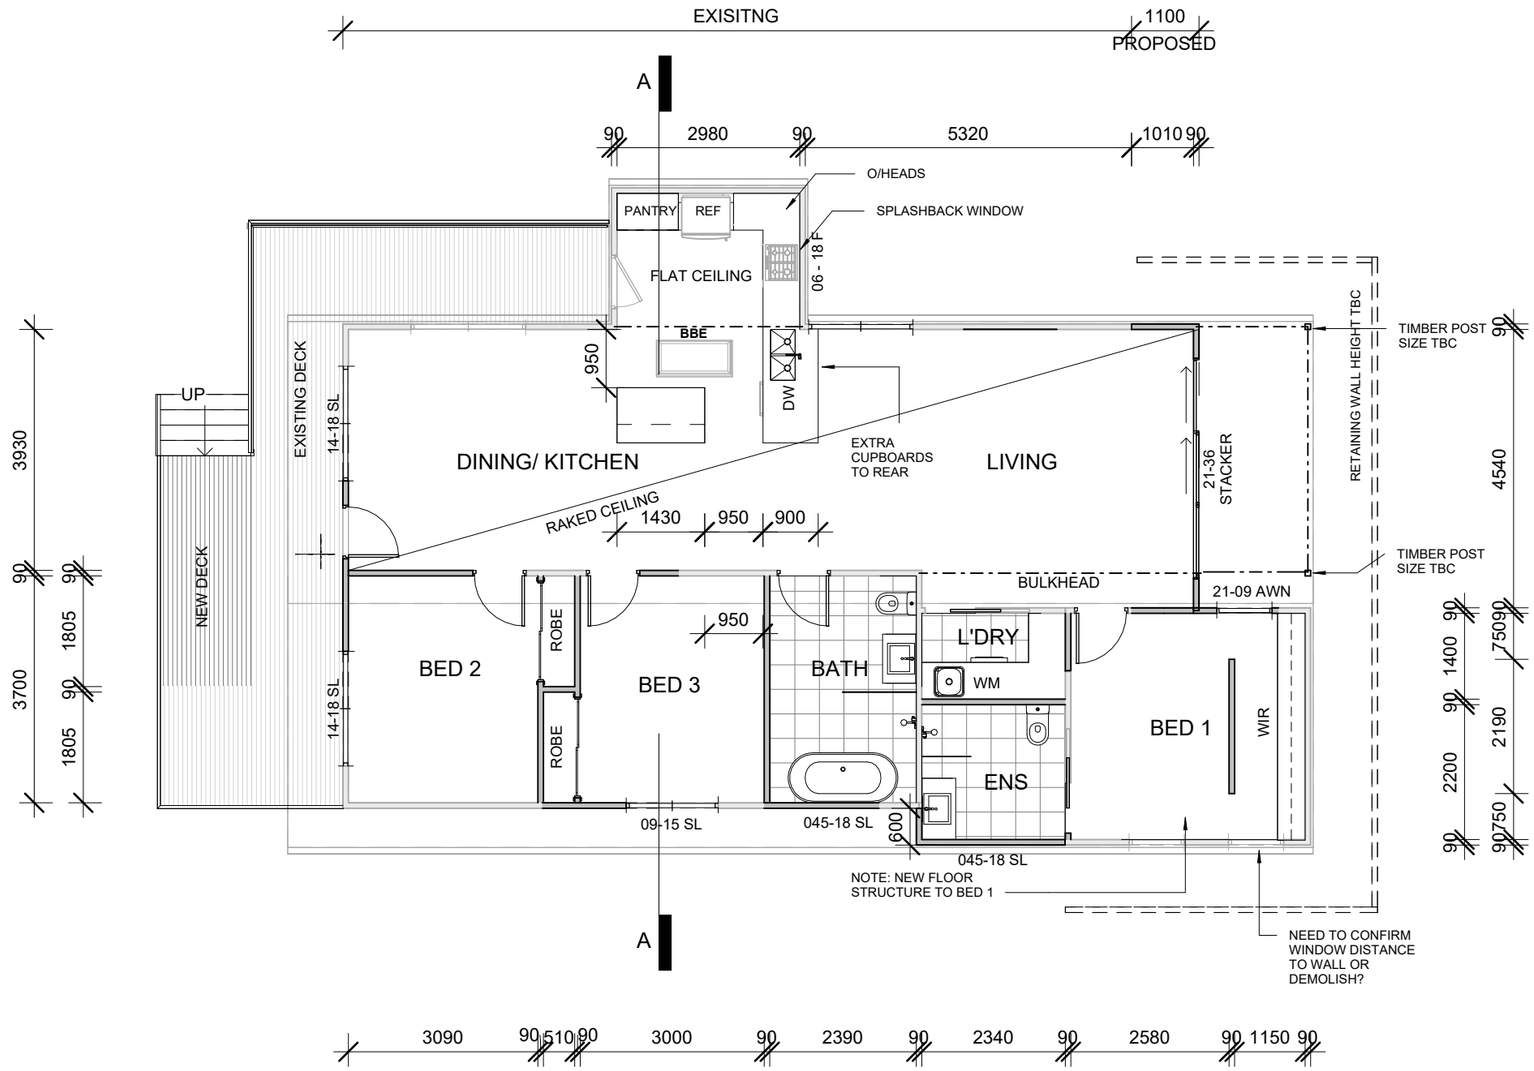

PROPOSED FLOOR PLAN

1 : 100

Address: REDACTED		**Design:** PROPOSED RENOVATION		Amendments		Date	Description
				Date	Description		
				13/08/2025	CONCEPT SKETCH		
Client:							
Date	13/08/2025	Page Size	A3 1 : 100				
Page Number	5.0 PROPOSED FLOOR PLAN	Drawings Prepared By	ND				

NOT FOR CONSTRUCTION

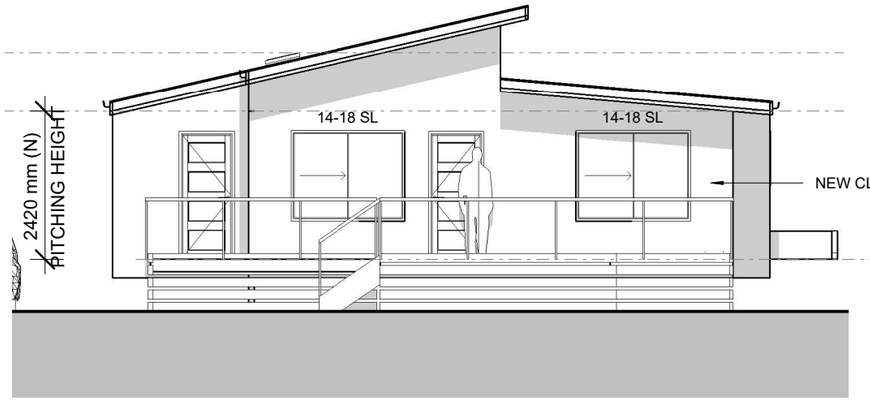

EAST ELEVATION - PROPOSED

1 : 100

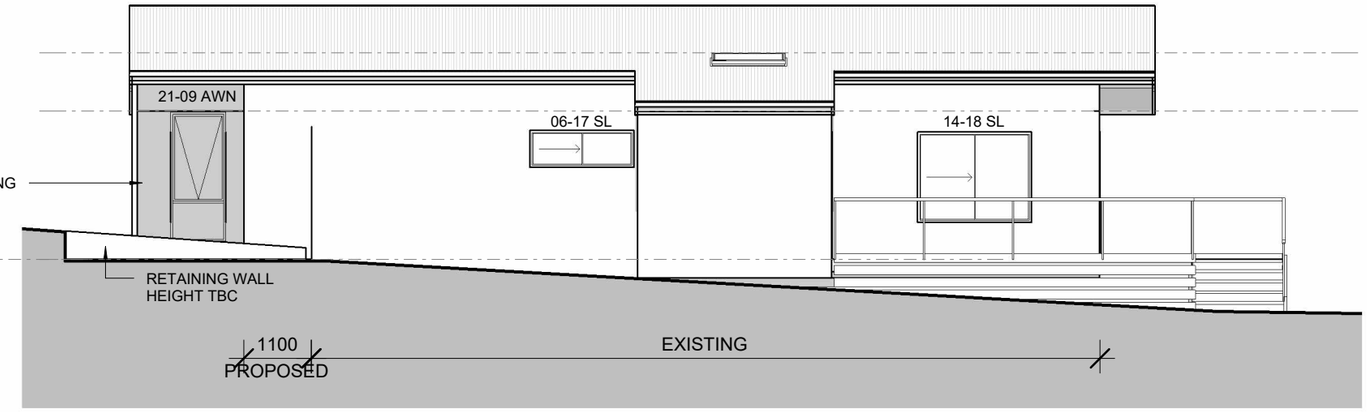

SOUTH ELEVATION - PROPOSED

1 : 100

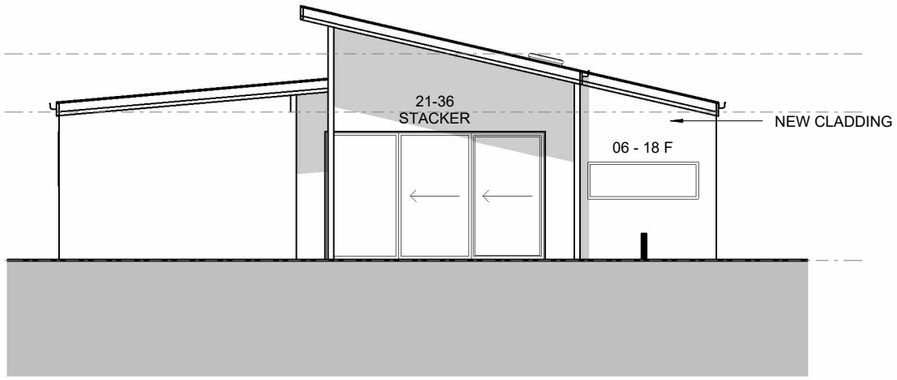

WEST ELEVATION - PROPOSED

1 : 100

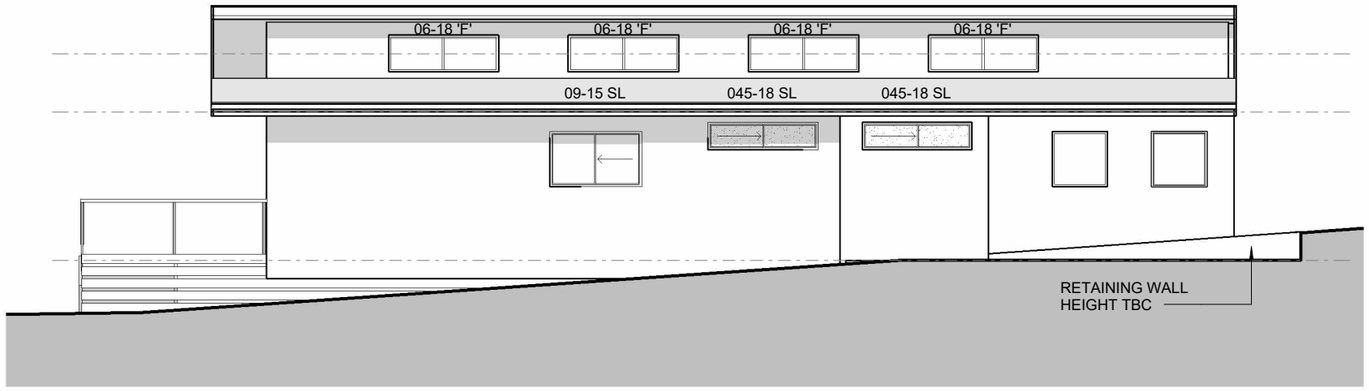

NORTH ELEVATION - PROPOSED

1 : 100

Address: REDACTED		**Design:** PROPOSED RENOVATION		Amendments		Date	Description
				Date	Description		
Client:				13/08/2025	CONCEPT SKETCH		
Date	13/08/2025	Page Size	A3 1 : 100				
Page Number	5.1 PROPOSED ELEVATIONS	Drawings Prepared By	ND				

NOT FOR CONSTRUCTION

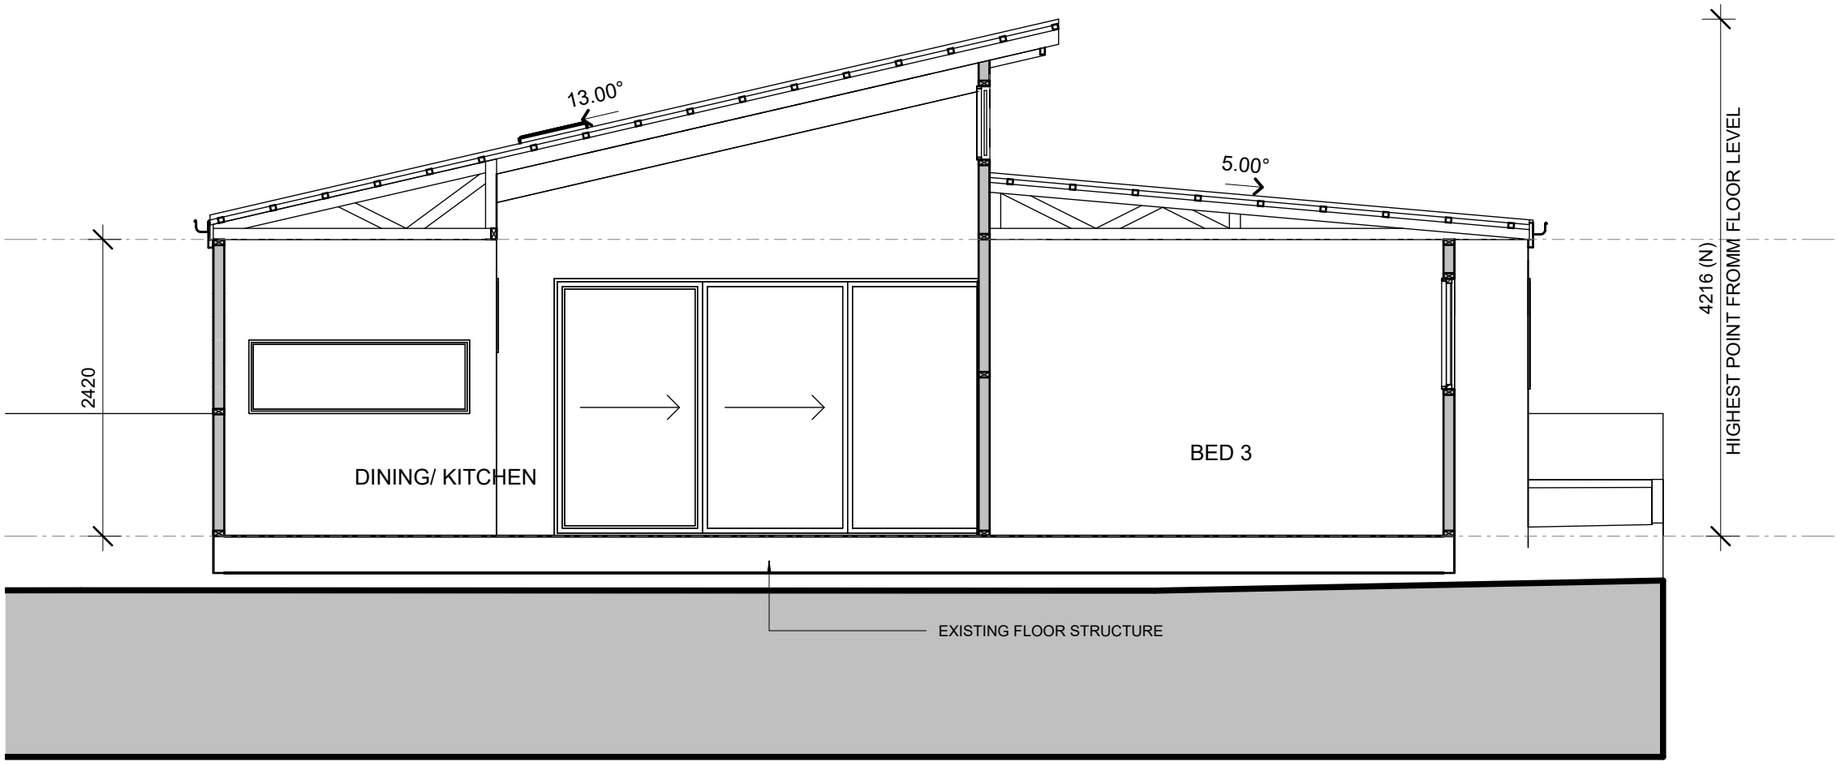

Section A-A

1 : 50

Address: REDACTED		**Design:** PROPOSED RENOVATION		Amendments		Date	Description
				Date	Description		
				13/08/2025	CONCEPT SKETCH		
Client:							
Date	13/08/2025	Page Size	A3 1 : 50				
Page Number	6.0 SECTION	Drawings Prepared By	ND				

NOT FOR CONSTRUCTION